


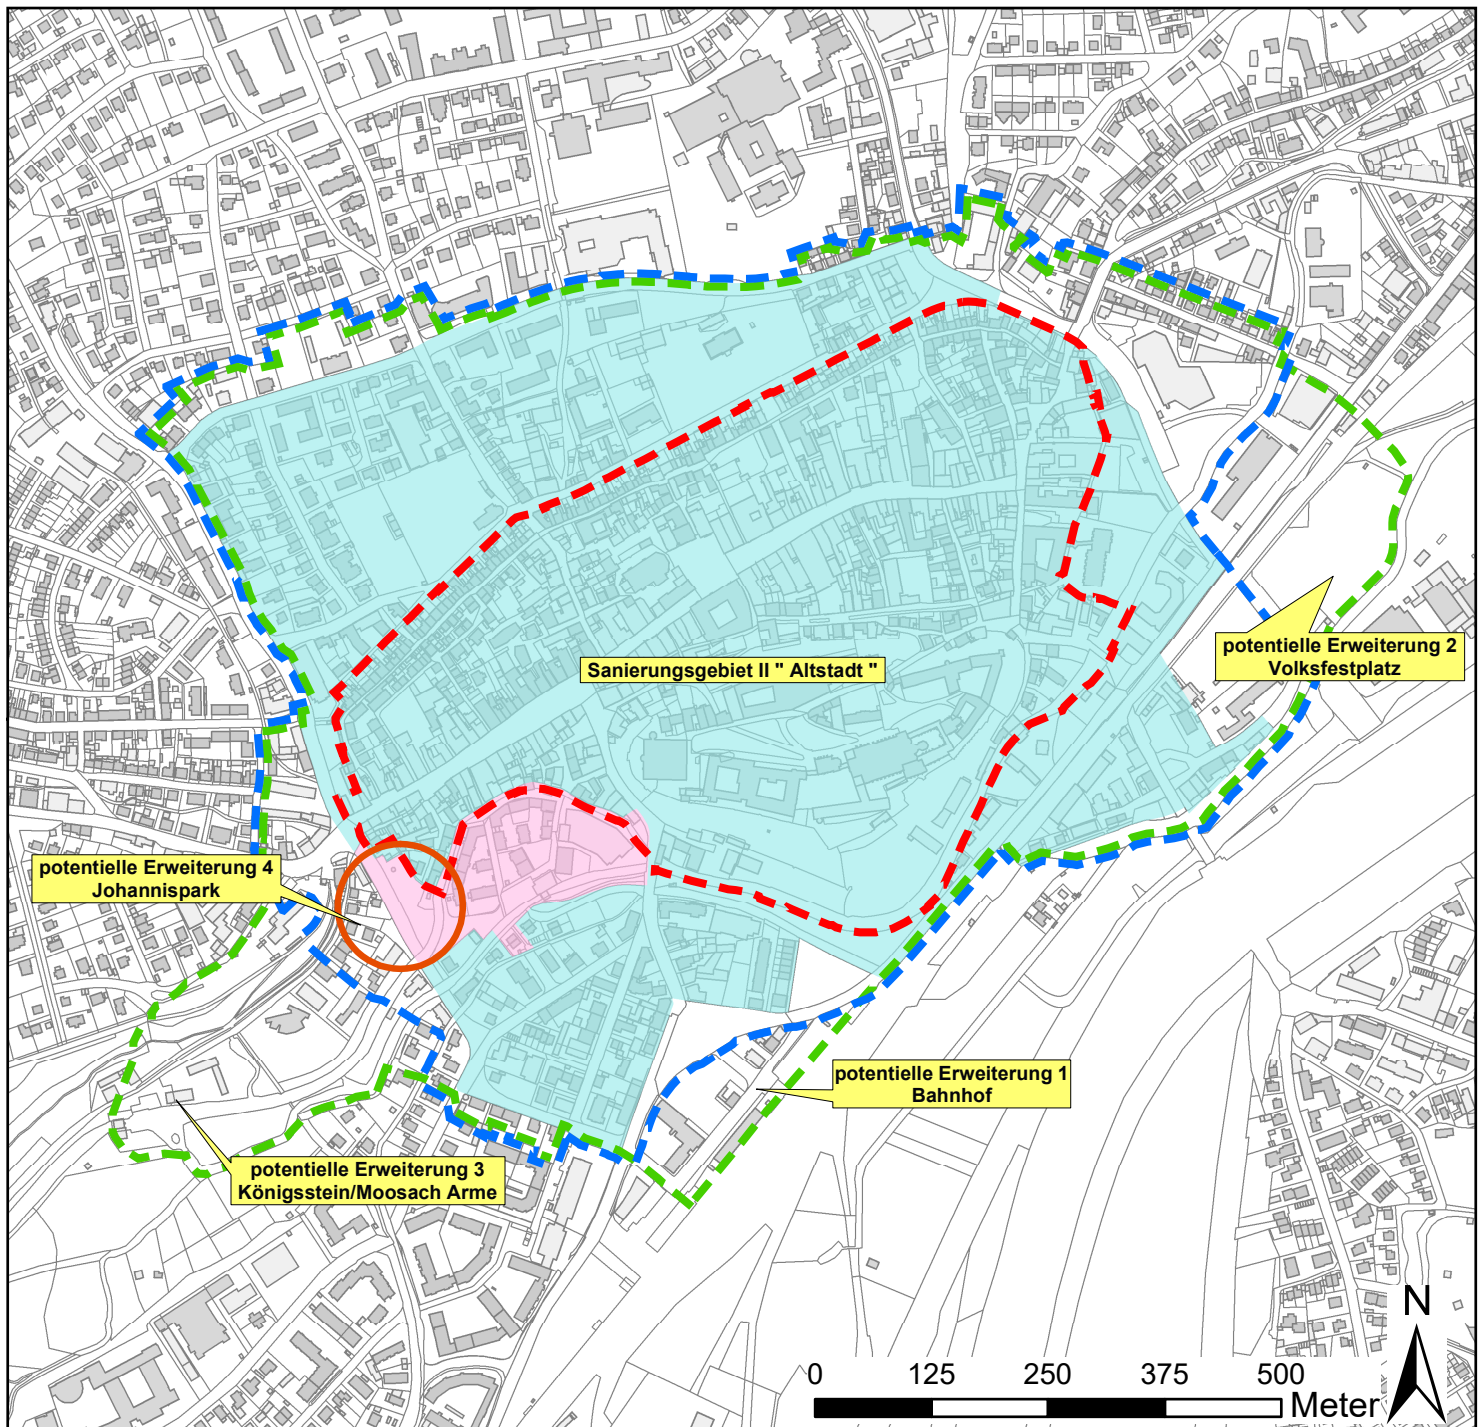

Sanierungsgebiet II - Altstadt (Altstadt und Domberg Freising mit den frühen Siedlungserweiterungen) - Untersuchungsgebiet

- Umgriff Sanierungssatzung I "Am Wörth"
- Umgriff Sanierungssatzung II "Altstadt"
- Ensemble Domberg und Altstadt Freising
- Abgrenzungsvorschlag nach dem Plan zur städtebaulichen Denkmalpflege
- Abgrenzungsvorschlag Stadt Freising